




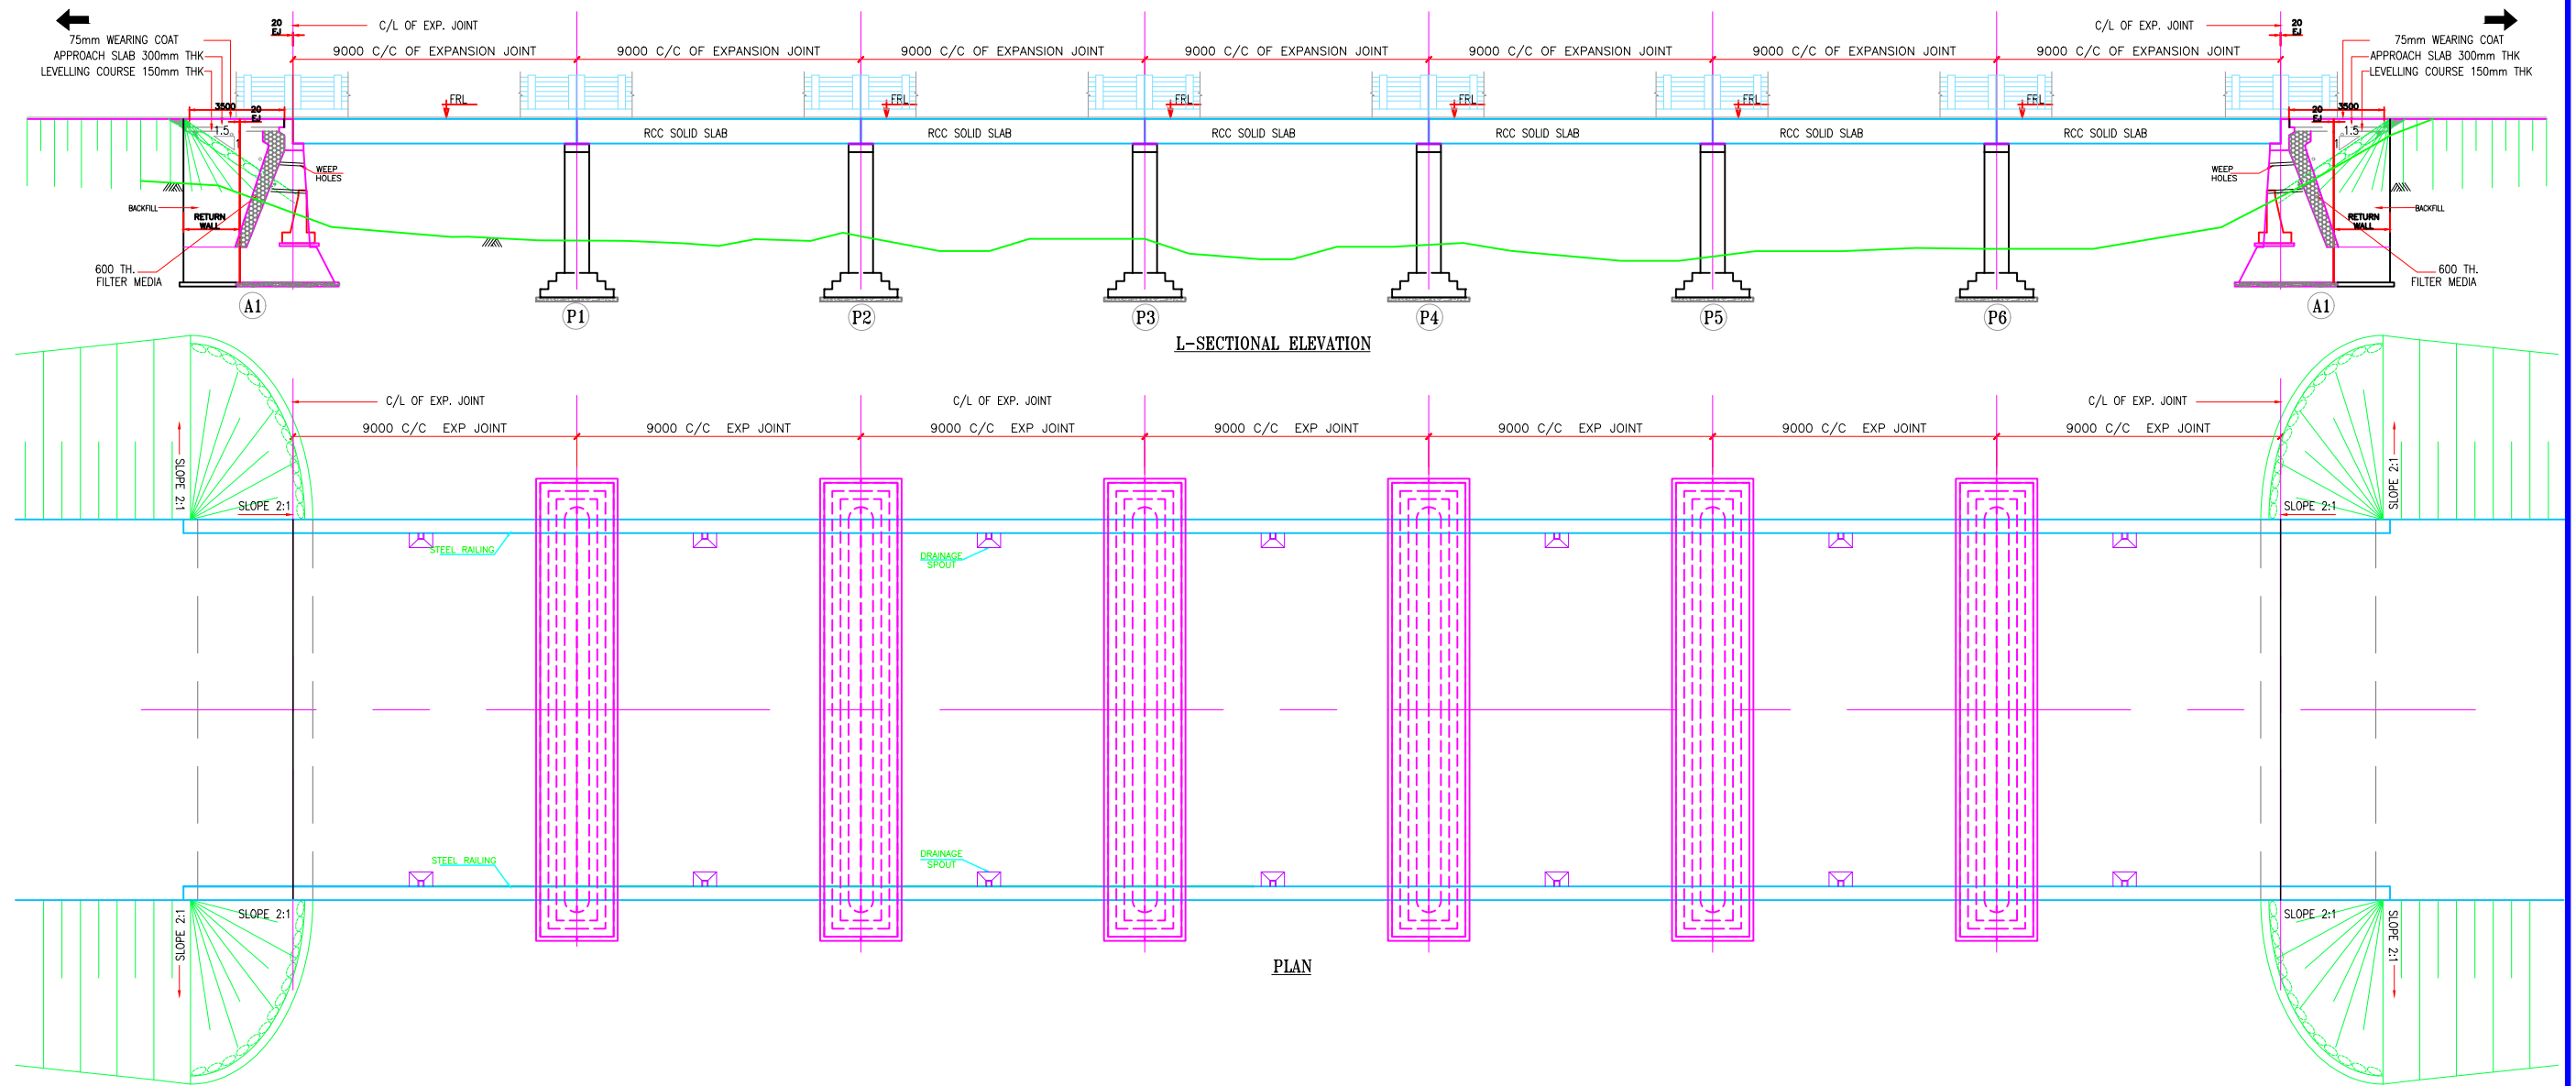




CONSULTANT :-	CLIENT :- Executive Engineer PMGSY, MRRDA Division Washim			ROAD NAME :- ODR 58 TO MALSUR TO RAJURA ANSING ROAD - BRIDGE CH 2300	DRAWING TITLE :- GENERAL ARRANGEMENT DRAWING OF MINOR BRIDGE OF SPAN 7x9.0 Mtr.	REVISION :-	R-00	DRAWING NO :-PMGSY/GAD/ 01			
		Deputy Engineer PMGSY, MRRDA DIVISION Washim	Executive Engineer PMGSY, MRRDA DIVISION Washim			SHEET :-	(01 OF 02)	SCALE :-	NTS	DATE :-	
						DRAWN BY :-		DESIGN BY:	-	APPROVED BY :-	

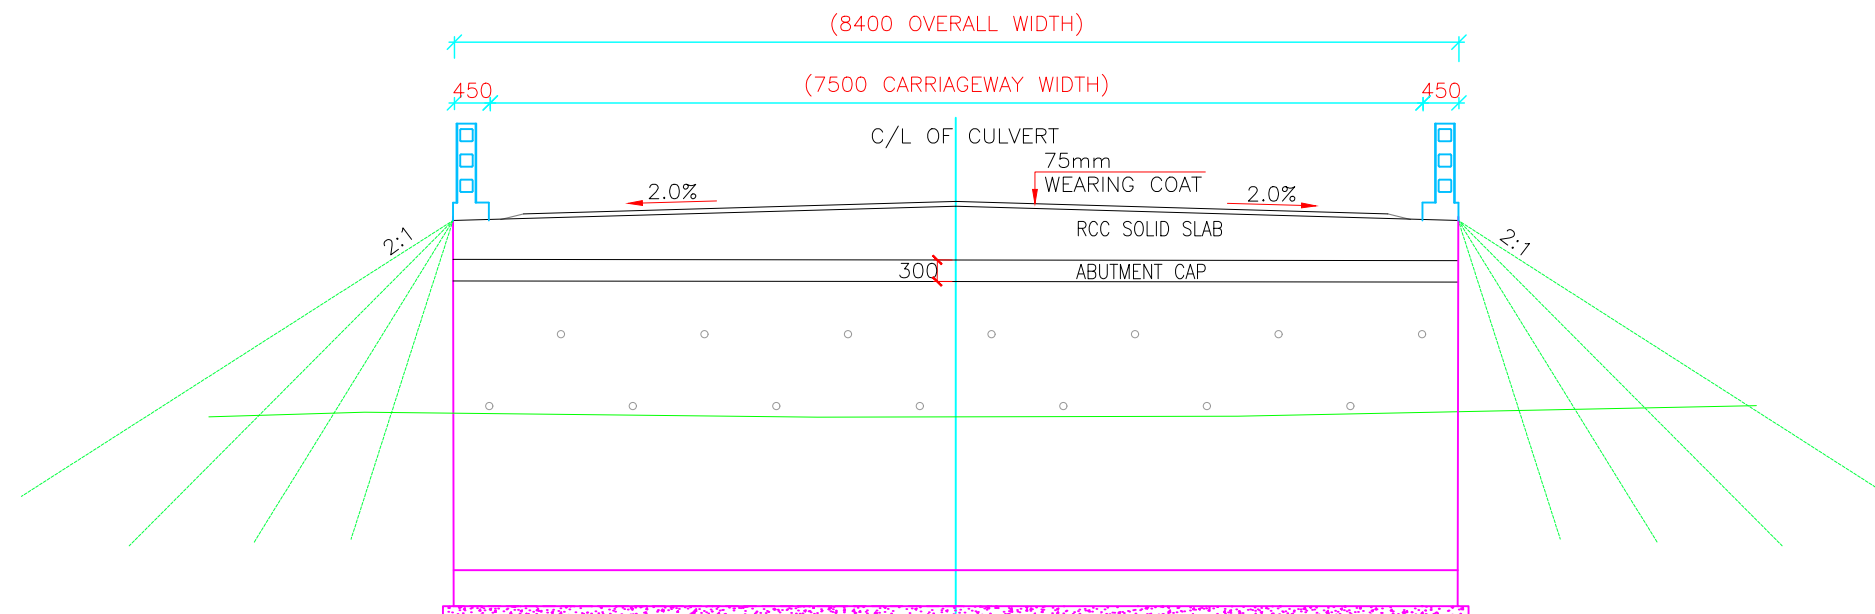

SECTION A-A

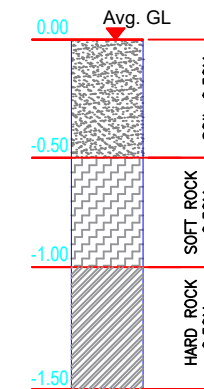

SOIL PROFILE

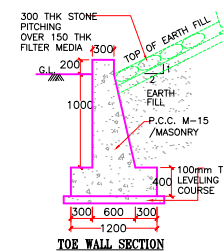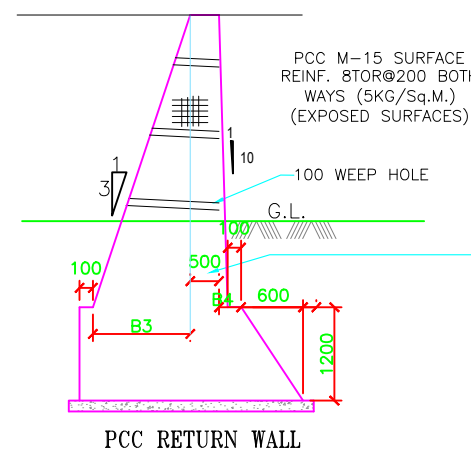
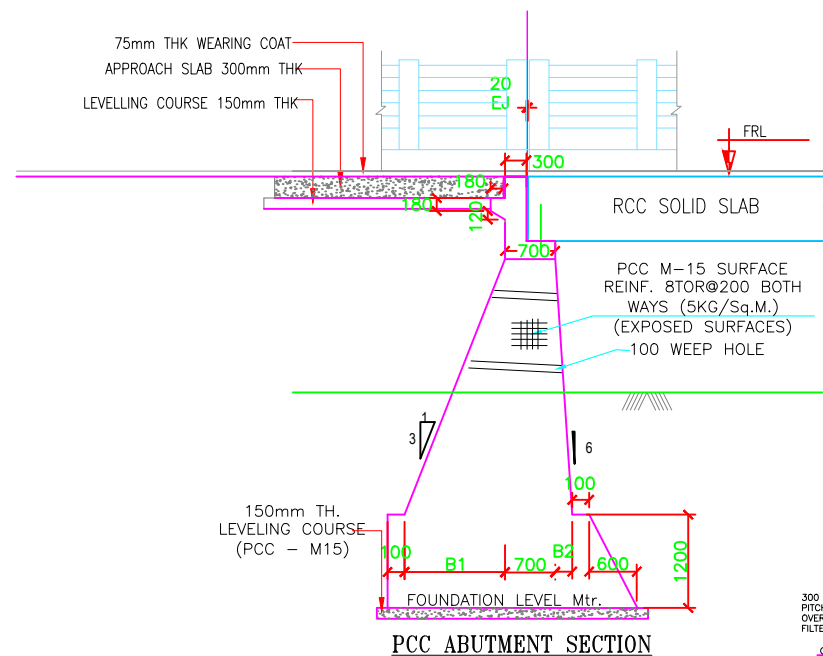


S. NO.	Chainage	TYPE OF PROPOSED STRUCTURE	FRL	BL	PROPOSAL	PROPOSED SPAN	HEIGHT	B1	B2	B3	B4
1	2+300	MINB (Slab)	102.625	97.610	Newproposed	7x9.0	5.015	1.90	0.95	2.25	0.67


NOTES:-

- ALL DIMENSIONS ARE IN MILLIMETERS UNLESS OTHERWISE SPECIFIED. LEVELS ARE IN METRES.
- DIMENSIONS ARE NOT TO BE SCALED. ONLY WRITTEN DIMENSIONS ARE TO BE FOLLOWED.
- GRADE OF CONCRETE :
PCC LEVELLING COURSE M-15 SLAB M-25
FOUNDATION PCC M-15 RETURN WALL PCC M-20
SUB STRUCTURE PCC M-20 APPROACH SLAB M-30
ABUTMENT CAP M-20
DIRT WALL M-20
- REINFORCEMENT H.Y.S.D. BARS CONFORMING TO IS:1786 GRADE Fe 500.
- BEARING TYPE : TAR PAPER
- THE BRIDGE HAS BEEN DESIGNED FOR CLASS A-3 LANE OR CLASS 70-R+CLASS A LOADING WHICH EVER PRODUCE WORST EFFECT.
- WEEP HOLES AT 1000 C/C BOTH HORIZONTALLY & VERTICALLY IN A STAGGERED MANNER IN ABUTMENT AND RETURN WALLS FROM BED LEVEL TO ABUTMENT CAP LEVEL.
- BACK FILL PARAMETERS ASSUMED ARE $C=0$, $\phi > 30^\circ$.
DRY DENSITY $= 18 \text{ kN/m}^3$
- FILLER TYPE EXPANSION JOINT SHALL BE PROVIDED AS PER MoRT&H SPECIFICATIONS.
- WEARING COAT SHALL BE 75mm THK CEMENT CONCRETE
- THE FOUNDATION DEPTH SHOULD BE MINIMUM 2m BELOW THE MAXIMUM SCOUR LEVEL. IF HARD ROCK IS ENCOUNTERED THE MINIMUM EMBEDMENT SHOULD BE 0.6m ON ALL SIDES OF THE FOOTING AND 1.5m IN THE CASE OF OTHER TYPE OF ROCKS AS PER REQUIREMENTS OF IRC 78.
- DRAINAGE SPOUT SHALL BE PROVIDED IN DECK SLAB AS PER MORTH.
- DISTANCE BETWEEN EXISTING KT WEIR AND PROPOSED BRIDGE IS 20.0 Mtr.


CONSULTANT :-	CLIENT :- Executive Engineer PMGSY, MRRDA Division Washim			ROAD NAME :- ODR 58 TO MALSUR TO RAJURA ANSING ROAD - BRIDGE CH 2300	DRAWING TITLE :- GENERAL ARRANGEMENT DRAWING OF MINOR BRIDGE OF SPAN 7x8.0 Mtr.	REVISION :-	R-00	DRAWING NO :-PMGSY/GAD/ 02			
		Deputy Engineer PMGSY, MRRDA DIVISION Washim	Executive Engineer PMGSY, MRRDA DIVISION Washim			SHEET :-	(02 OF 02)	SCALE :-	NTS	DATE :-	
						DRAWN BY :-		DESIGN BY:	-	APPROVED BY :-	

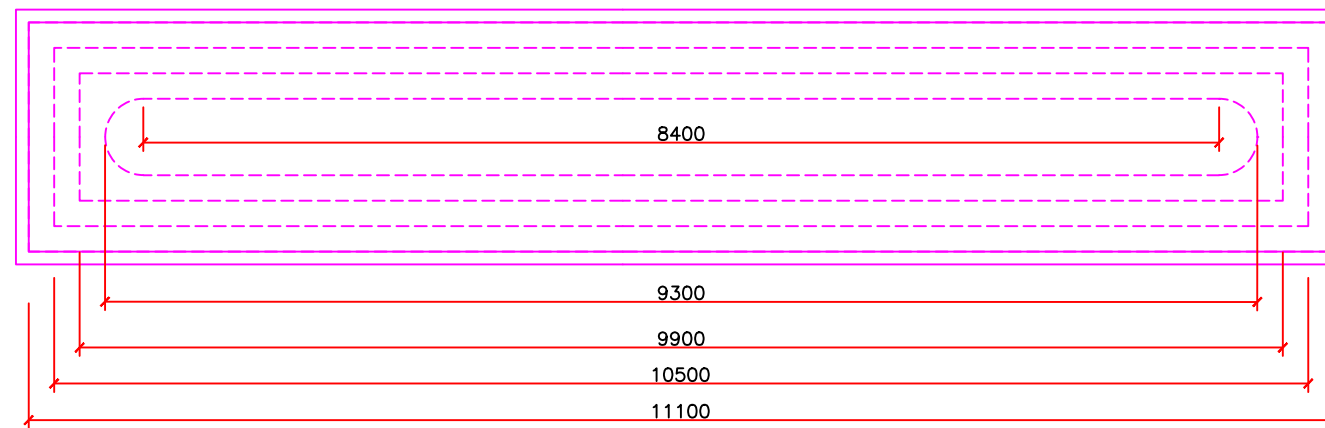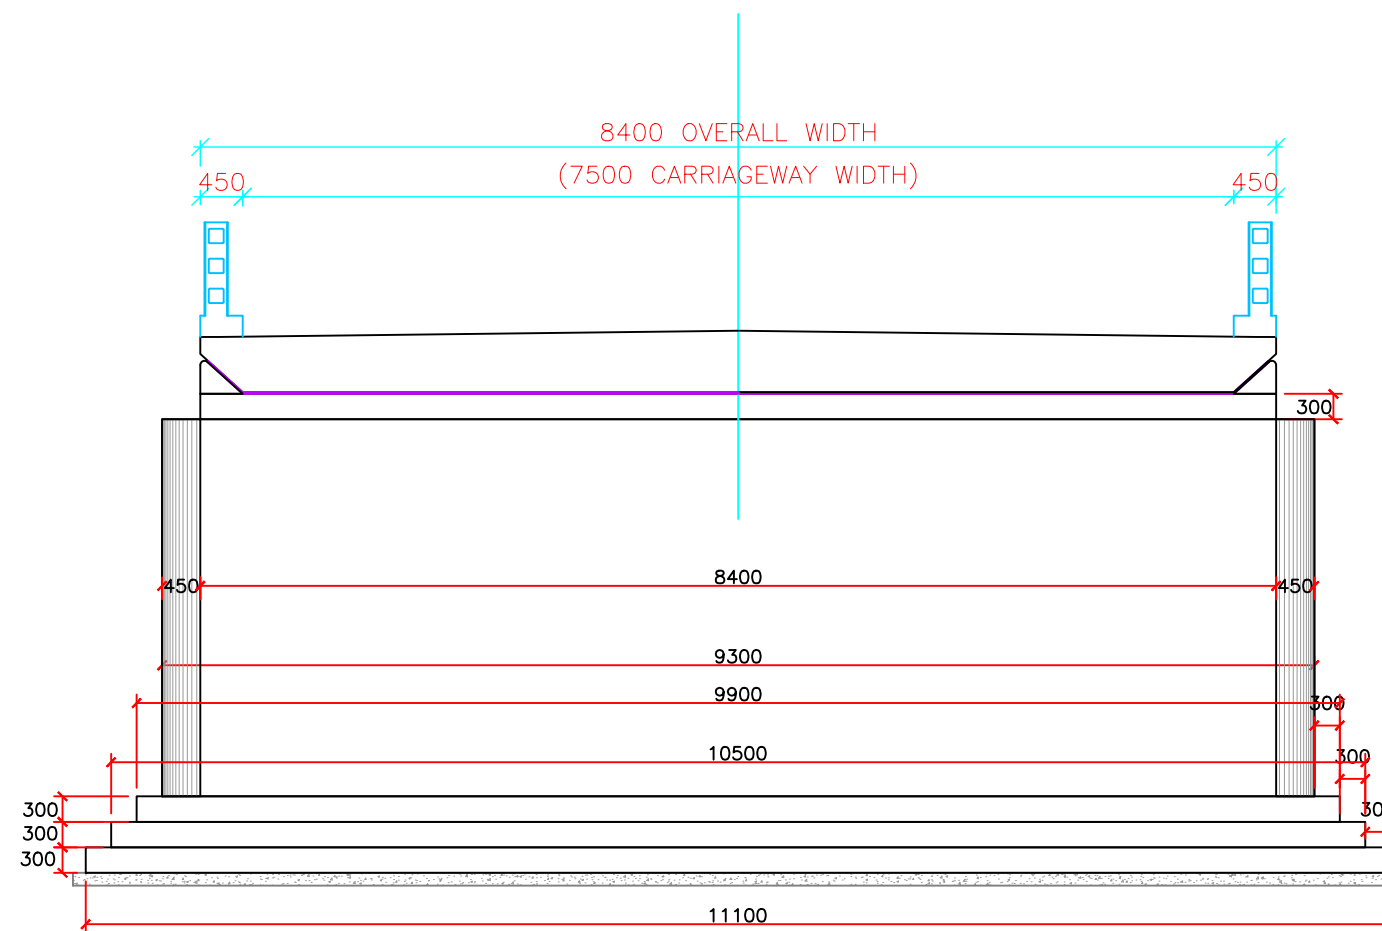

PCC PIER PLAN

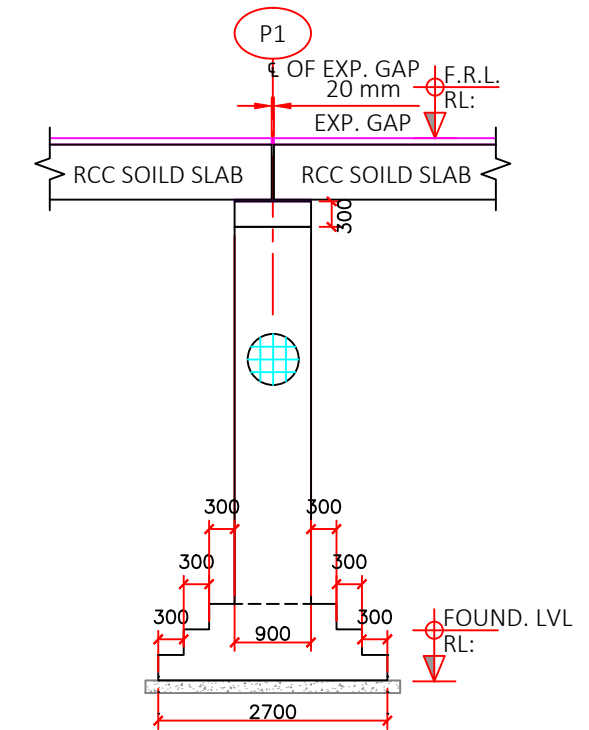

PCC PIER SECTION

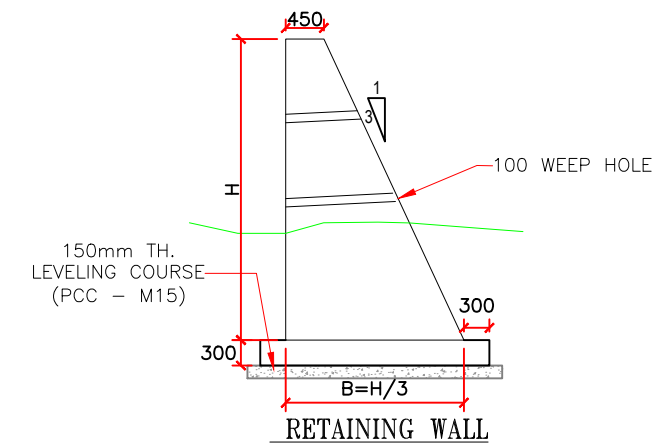

RETAINING WALL

CONSULTANT :-	CLIENT :- Executive Engineer PMGSY, MRRDA Division Washim			ROAD NAME :- ODR 58 TO MALSUR TO RAJURA ANSING ROAD - BRIDGE CH 2300	DRAWING TITLE :- GENERAL ARRANGEMENT DRAWING OF MINOR BRIDGE OF SPAN 7x8.0 Mtr.	REVISION :-	R-00	DRAWING NO :-PMGSY/GAD/ 02			
		Deputy Engineer PMGSY, MRRDA DIVISION Washim	Executive Engineer PMGSY, MRRDA DIVISION Washim			SHEET :-	(02 OF 02)	SCALE :-	NTS	DATE :-	
						DRAWN BY :-		DESIGN BY:	-	APPROVED BY :-	